

CLOBEK HERITAGE PLACE,

LUGBE

PROPOSED RESIDENTIAL DEV.@

PLOT 1946 SABON-LUGBE EAST EXTENSION LAYOUT, LUGBE, ABUJA, F.C.T.


CLOBEK NIG. LTD.

PRESENTATION DRAWING

SPACEMERGE®
DESIGNS

SPACEMERGE
RC 2714237
Number 31, GBAZANGO EXTENSION,
KUBWA, BWARI AREA COUNCIL
F.C.T.
support@spacemerge.com

APRIL,2026

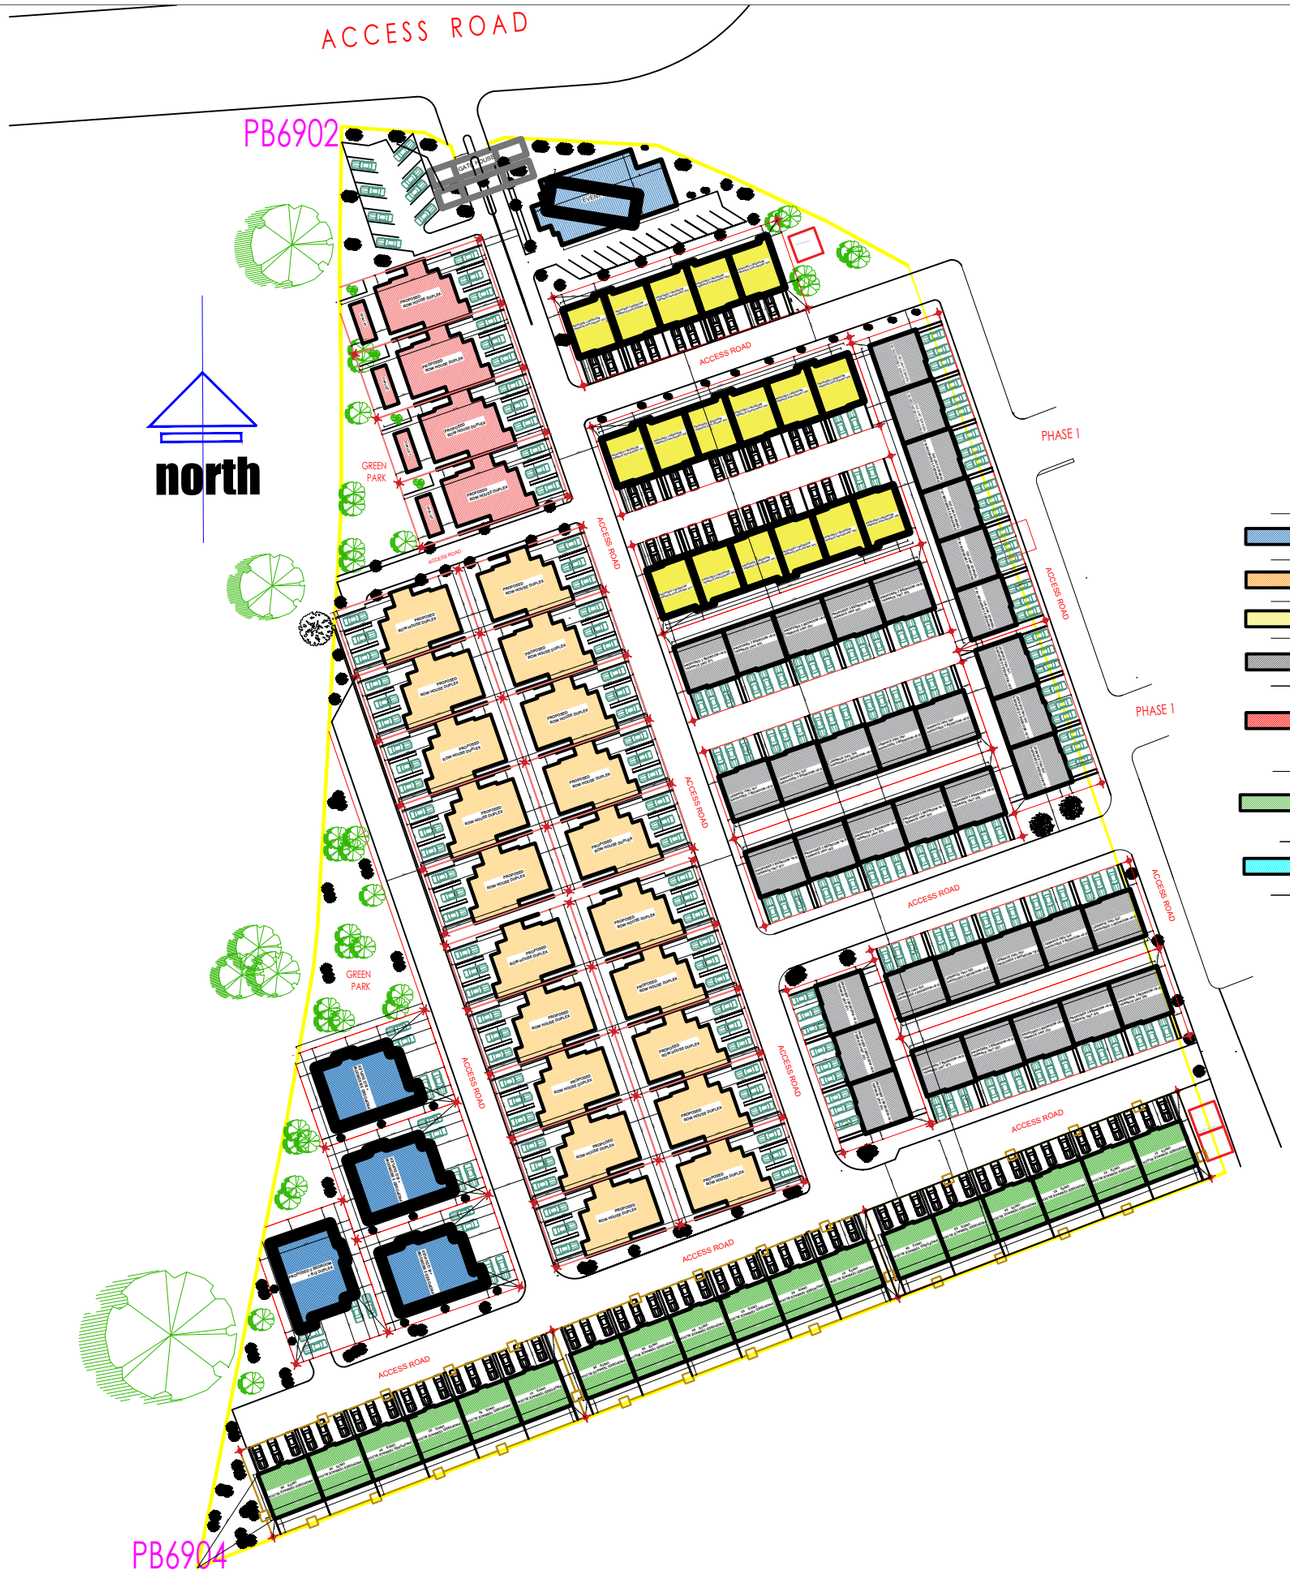

LEGEND

BUILDING TYPE	NUMBERS	
5 BEDROOM+ B.Q DUPLEX (STAND ALONE HOUSES)	4 UNITS	PROTOYPE 6
4 BEDROOM + B.Q DUPLEX (ROW HOUSES)	20 UNITS	PROTOYPE 4
3 BEDROOM TERRACE DUPLEX	3 BLOCKS (17 UNITS)	PROTOYPE 1
3 BEDROOM + B.Q TERRACE DUPLEX	8 BLOCKS (37 UNITS)	PROTOYPE 2
4 BEDROOM + B.Q DUPLEX & GUEST CHALLET (ROW HOUSES)	4 UNITS	PROTOYPE 5
4 BEDROOM + B.Q TERRACE DUPLEX	8 BLOCKS (37 UNITS)	PROTOYPE 3
EVENT CENTER		

SITE PLAN

SPACEMERGE® DESIGNS

CLOBEK HERITAGE PLACE,

PROPOSED RESIDENTIAL DEV. @PLOT 1914 SABON-LUGBE EAST EXTENSION,LUGBE,ABUJA

CLOBEK NIG, LTD

NOTES:
1. Do not scale drawings, use figured dimensions only.
2. All dimensions are given in Metric System and to the nearest millimeter (mm).
3. Any discrepancy on site should be referred to the Architect for clarification before proceeding with new works.
4. 4 Architectural Drawings to be read in conjunction with relevant Engineering Drawings.
5. Standard of Constructions should conform with Architect's and Engineer's Specifications.
6. All critical construction stages should be approved by the Architect or Engineer as relevant.
7. Schedule of Finishes and other Specifications are to be used with these Architectural Drawings. - Refer any discrepancies to the Architect.

DRW: EDISON | CHECK: SHLOM | SPACE/2026/04/CH..09

OCTOBER 5, 2022

A 208



SITE PLOT IMAGE

SPACEMERGE® DESIGNS

CLOBEK HERITAGE PLACE,

PROPOSED RESIDENTIAL DEV. @PLOT 1914 SABON-LUGBE EAST EXTENSION,LUGBE,ABUJA

CLOBEK NIG, LTD

NOTES:
1. Do not scale drawings, use figured dimensions only.
2. All dimensions are given in Metric System and to the nearest millimeter (mm).
3. Any discrepancy on site should be referred to the Architect for clarification before proceeding with new works.
4. 4 Architectural Drawings to be read in conjunction with relevant Engineering Drawings.
5. Standard of Constructions should conform with Architect's and Engineer's Specifications.
6. All critical construction stages should be approved by the Architect or Engineer as relevant.
7. Schedule of Finishes and other Specifications are to be used with these Architectural Drawings. - Refer any discrepancies to the Architect.

SPACE/2026/04/CH..09 | DRW: EDISON | CHECK: SHLOMO | OCTOBER 5, 2022 | A 208

PROTOTYPE 03

4 BEDROOM + B.Q TERRACE DUPLEX

NO. OF UNITS =18 UNITS

SIZE PER PLOT = 167 SQM

CAR PARK(S) = 3 CARS

03
1:100

DRW: EDISON | CHECK: SHLOM | SPACE/2026/04/CH..09

OCTOBER 5, 2022

A103


SPACEMERGE® DESIGNS

CLOBEK HERITAGE PLACE,

PROPOSED RESIDENTIAL DEV. @PLOT 1914 SABON-LUGBE EAST EXTENSION,LUGBE,ABUJA

CLOBEK NIG, LTD

NOTES:
1. Do not scale drawings, use figured dimensions only.
2. All dimensions are given in Metric System and to the nearest millimeter (mm).
3. Any discrepancy on site should be referred to the Architect for clarification before proceeding with new works.
4. 4 Architectural Drawings to be read in conjunction with relevant Engineering Drawings.
5. Standard of Constructions should conform with Architect's and Engineer's Specifications.
6. All critical construction stages should be approved by the Architect or Engineer as relevant.
7. Schedule of Finishes and other Specifications are to be used with these Architectural Drawings. - Refer any discrepancies to the Architect.

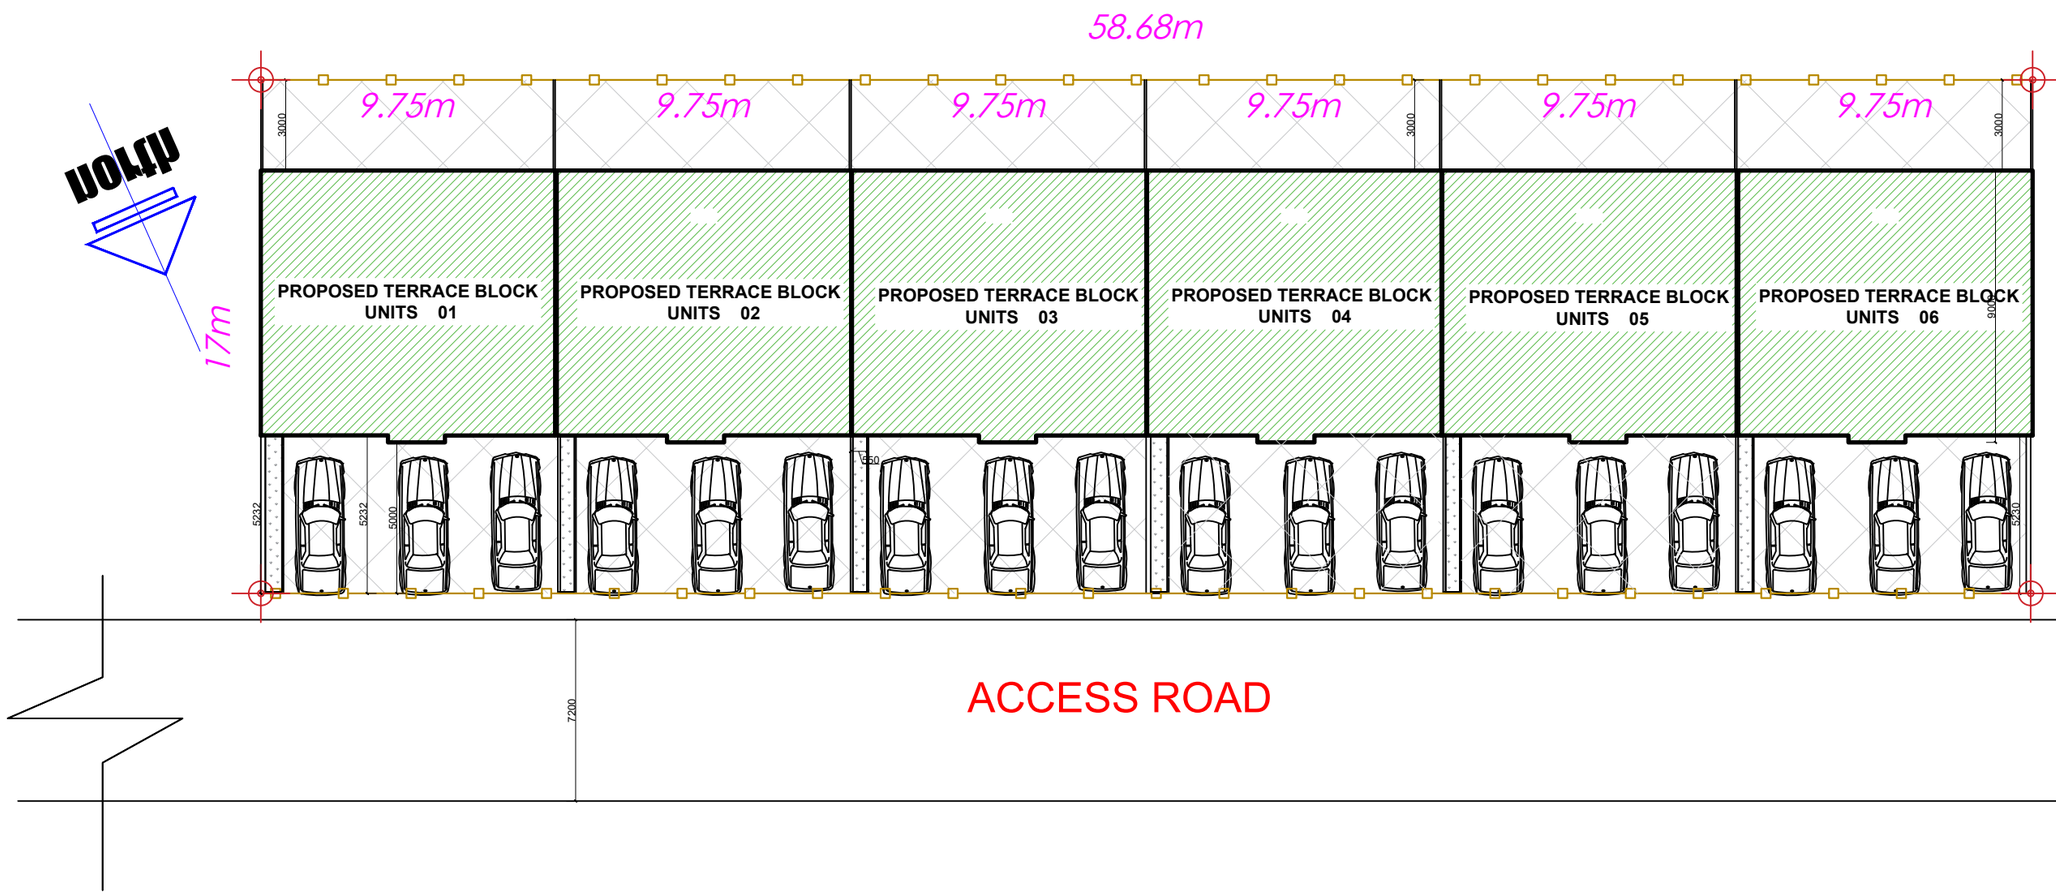

PARAMETERS	
Site Area	997.60 Sqm
Unit Area	86.0 Sqm
Plot size	167.0 Sqm
Built Area	516.0 Sqm
%Un-built	48.30%

PROTOTYPE 3 SITE PLAN

1:100

SPACEMERGE® DESIGNS

CLOBEK HERITAGE PLACE,

PROPOSED RESIDENTIAL DEV. @PLOT 1914 SABON-LUGBE EAST EXTENSION,LUGBE,ABUJA


CLOBEK NIG, LTD

NOTES:
1. Do not scale drawings, use figured dimensions only.
2. All dimensions are given in Metric System and to the nearest millimeter (mm).
3. Any discrepancy on site should be referred to the Architect for clarification before proceeding with new works.
4. 4 Architectural Drawings to be read in conjunction with relevant Engineering Drawings.
5. Standard of Constructions should conform with Architect's and Engineer's Specifications.
6. All critical construction stages should be approved by the Architect or Engineer as relevant.
7. Schedule of Finishes and other Specifications are to be used with these Architectural Drawings. - Refer any discrepancies to the Architect.

CHECK: SHLOM | SPACE/2026/04/CH..09

DRW: EDISON | OCTOBER 5, 2022

A103

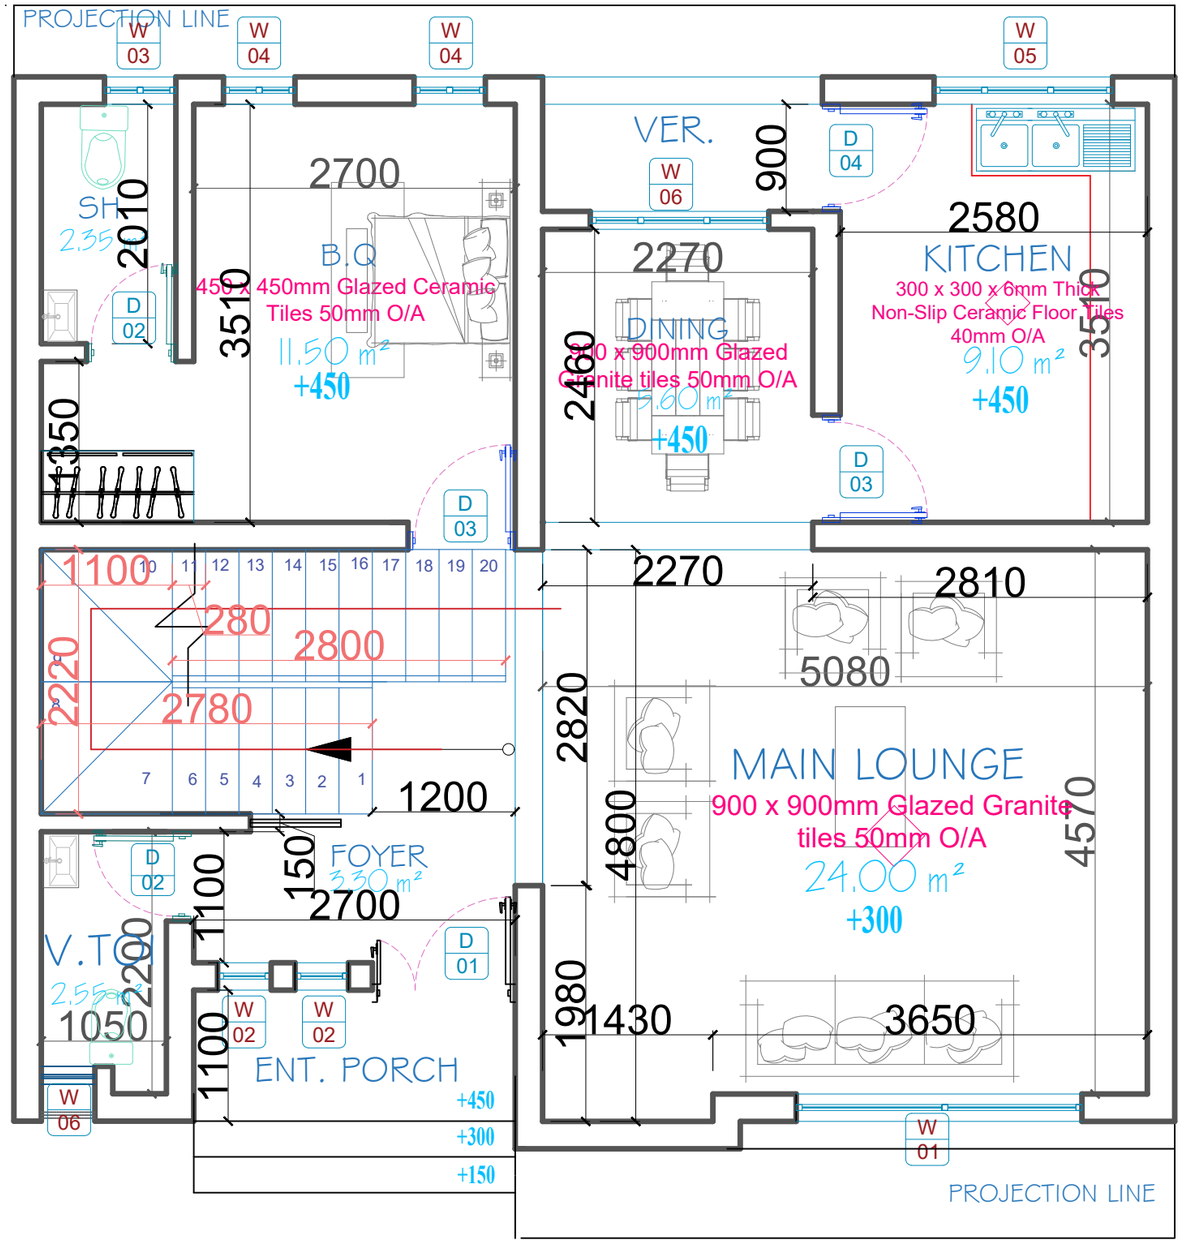

GROUND FLOOR (4 BED + B.Q TERRACE DUPLEX)

1:100

SPACEMERGE® DESIGNS

CLOBEK HERITAGE PLACE,

PROPOSED RESIDENTIAL DEV. @PLOT 1914 SABON-LUGBE EAST EXTENSION,LUGBE,ABUJA


CLOBEK NIG, LTD

NOTES:
1. Do not scale drawings, use figured dimensions only.
2. All dimensions are given in Metric System and to the nearest millimeter (mm).
3. Any discrepancy on site should be referred to the Architect for clarification before proceeding with new works.
4. 4 Architectural Drawings to be read in conjunction with relevant Engineering Drawings.
5. Standard of Constructions should conform with Architect's and Engineer's Specifications.
6. All critical construction stages should be approved by the Architect or Engineer as relevant.
7. Schedule of Finishes and other Specifications are to be used with these Architectural Drawings. - Refer any discrepancies to the Architect.

DRW: EDISON | CHECK: SHLOM | SPACE/2026/04/CH..09

OCTOBER 5, 2022

A 102

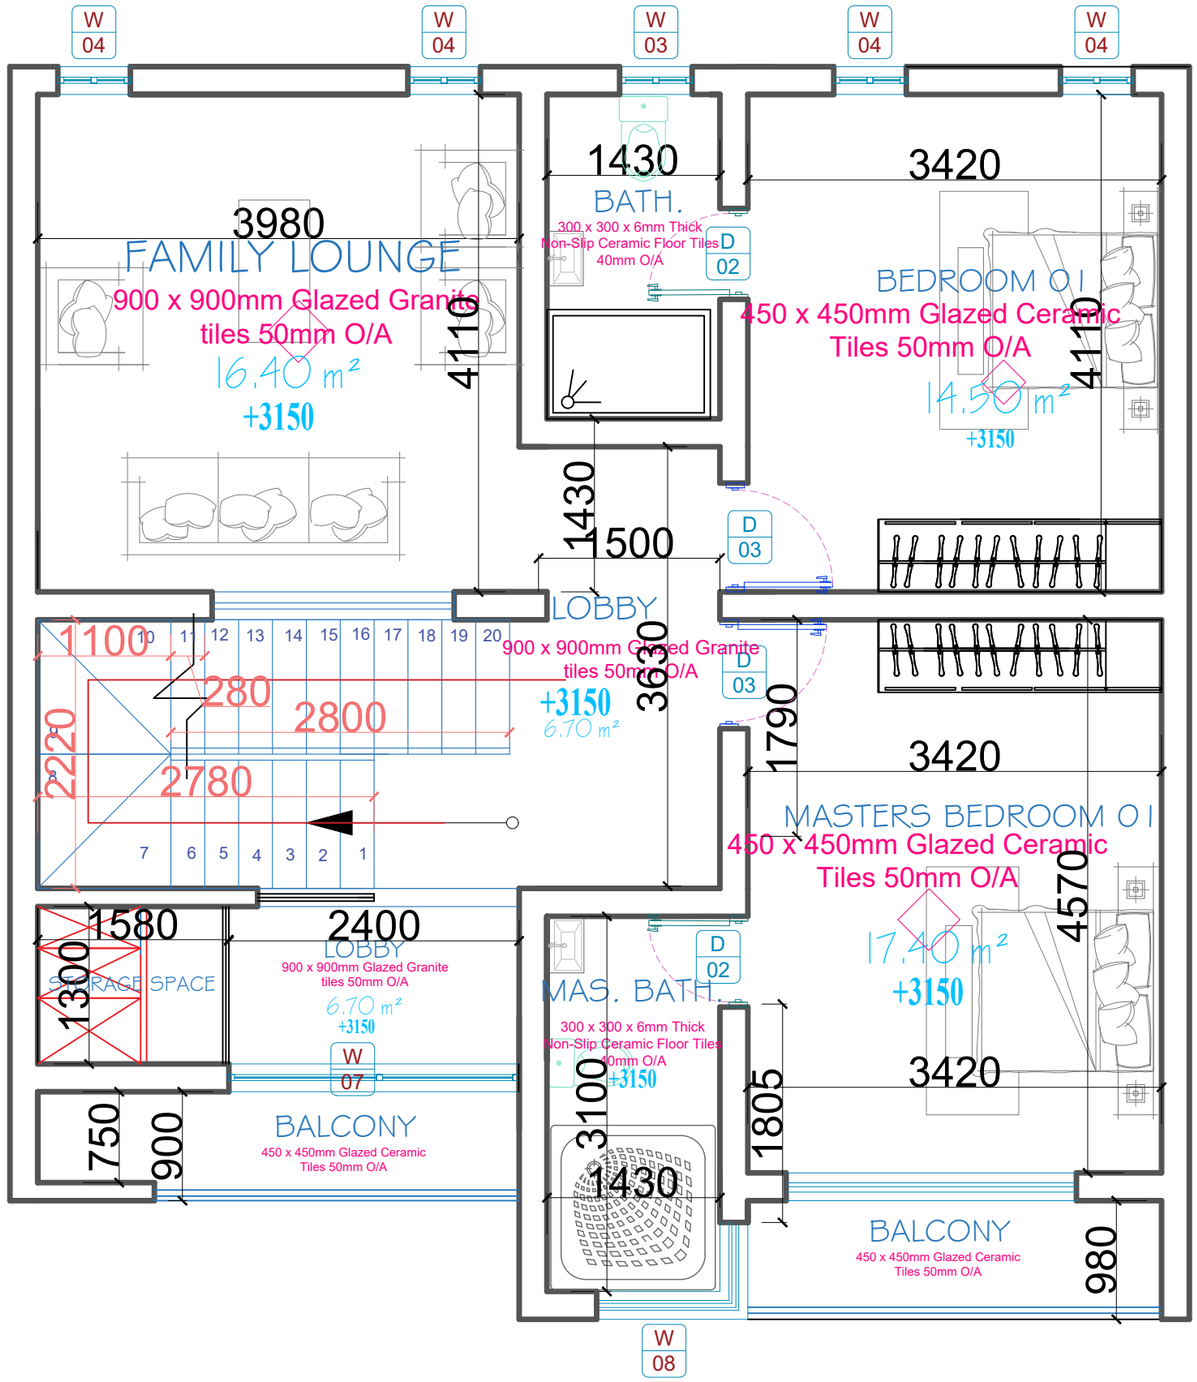

FIRST FLOOR (4 BED + B.Q TERRACE DUPLEX)

1:100

SPACEMERGE® DESIGNS

CLOBEK HERITAGE PLACE,

PROPOSED RESIDENTIAL DEV. @PLOT 1914 SABON-LUGBE EAST EXTENSION,LUGBE,ABUJA


CLOBEK NIG, LTD

NOTES:
1. Do not scale drawings, use figured dimensions only.
2. All dimensions are given in Metric System and to the nearest millimeter (mm).
3. Any discrepancy on site should be referred to the Architect for clarification before proceeding with new works.
4. 4 Architectural Drawings to be read in conjunction with relevant Engineering Drawings.
5. Standard of Constructions should conform with Architect's and Engineer's Specifications.
6. All critical construction stages should be approved by the Architect or Engineer as relevant.
7. Schedule of Finishes and other Specifications are to be used with these Architectural Drawings. - Refer any discrepancies to the Architect.

DRW: EDISON | CHECK: SHLOM | SPACE/2026/04/CH..09

SEPTEMBER 14, 2025

A106

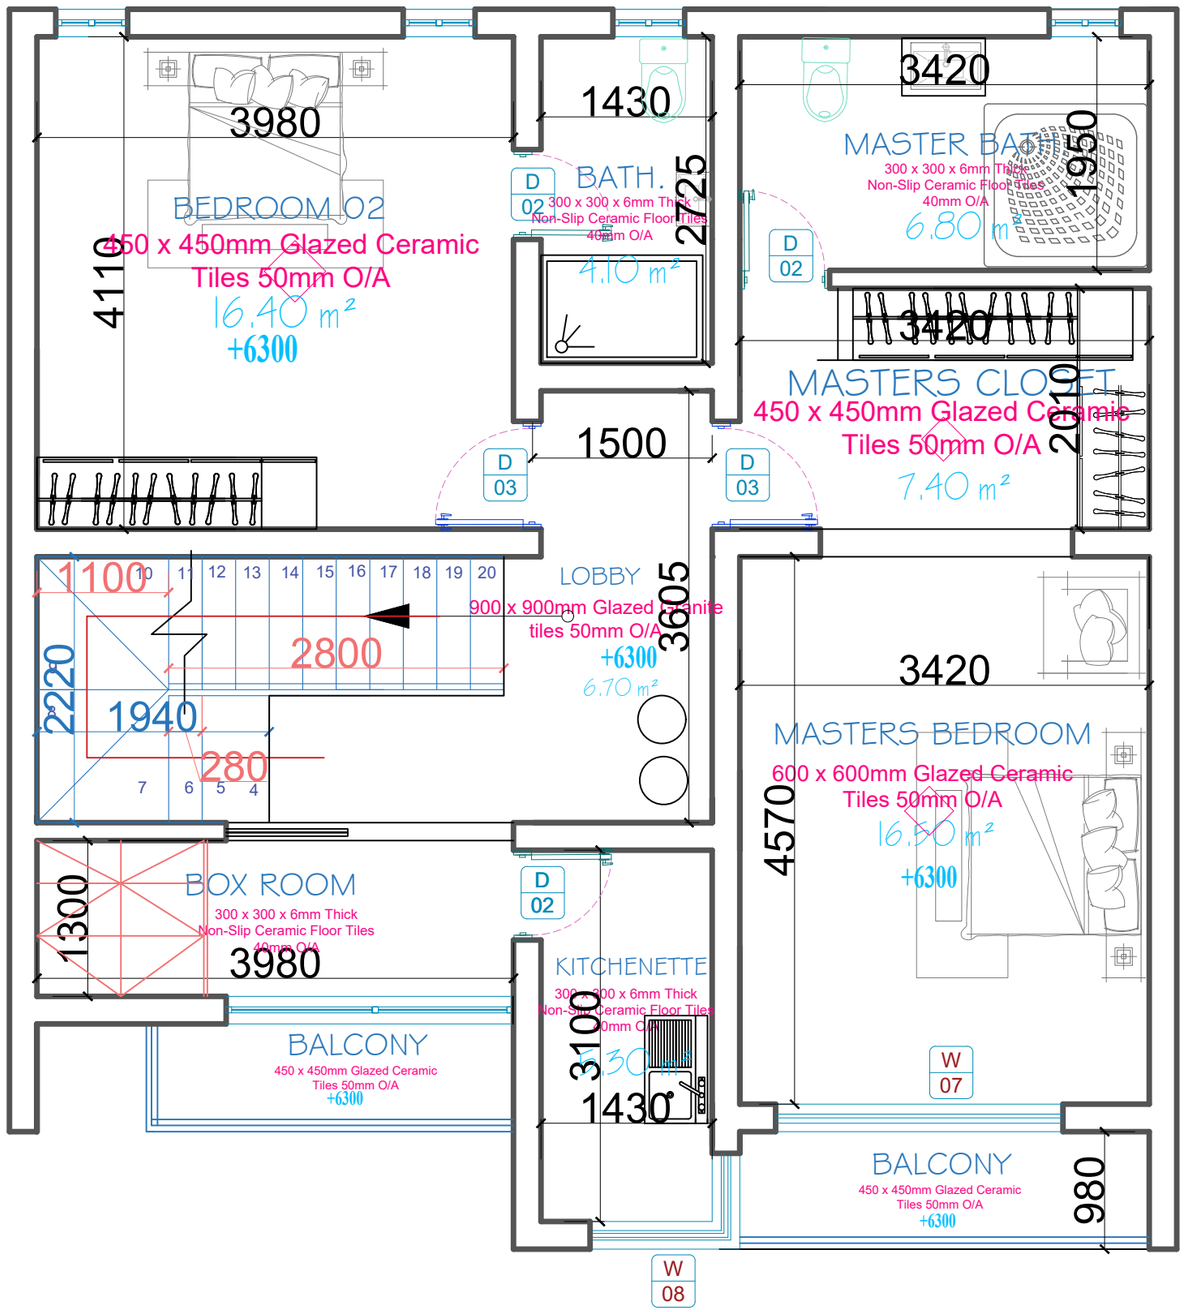

SECOND FLOOR (4 BED + B.Q TERRACE DUPLEX)

1:100

SPACEMERGE® DESIGNS

CLOBEK HERITAGE PLACE,

PROPOSED RESIDENTIAL DEV. @PLOT 1914 SABON-LUGBE EAST EXTENSION,LUGBE,ABUJA

CLOBEK NIG, LTD

NOTES:
1. Do not scale drawings, use figured dimensions only.
2. All dimensions are given in Metric System and to the nearest millimeter (mm).
3. Any discrepancy on site should be referred to the Architect for clarification before proceeding with new works.
4. 4 Architectural Drawings to be read in conjunction with relevant Engineering Drawings.
5. Standard of Constructions should conform with Architect's and Engineer's Specifications.
6. All critical construction stages should be approved by the Architect or Engineer as relevant.
7. Schedule of Finishes and other Specifications are to be used with these Architectural Drawings. - Refer any discrepancies to the Architect.

DRW: EDISON | CHECK: SHLOM | SPACE/2026/04/CH..09

SEPTEMBER 14, 2025

A106



IMAGE 05
1:50

SPACEMERGE® DESIGNS

CLOBEK HERITAGE PLACE,

PROPOSED RESIDENTIAL DEV. @PLOT 1914 SABON-LUGBE EAST EXTENSION,LUGBE,ABUJA

CLOBEK NIG, LTD

NOTES:
1. Do not scale drawings, use figured dimensions only.
2. All dimensions are given in Metric System and to the nearest millimeter (mm).
3. Any discrepancy on site should be referred to the Architect for clarification before proceeding with new works.
4. 4 Architectural Drawings to be read in conjunction with relevant Engineering Drawings.
5. Standard of Constructions should conform with Architect's and Engineer's Specifications.
6. All critical construction stages should be approved by the Architect or Engineer as relevant.
7. Schedule of Finishes and other Specifications are to be used with these Architectural Drawings. - Refer any discrepancies to the Architect.

DRW: EDISON | CHECK: SHLOM | SPACE/2026/04/CH..09

OCTOBER 5, 2022

A 102





IMAGE 06
1:50

CLOBEK HERITAGE PLACE,

PROPOSED RESIDENTIAL DEV. @PLOT 1914 SABON-LUGBE EAST EXTENSION,LUGBE,ABUJA

CLOBEK NIG, LTD

SPACEMERGE® DESIGNS

NOTES:
1. Do not scale drawings, use figured dimensions only.
2. All dimensions are given in Metric System and to the nearest millimeter (mm).
3. Any discrepancy on site should be referred to the Architect for clarification before proceeding with new works.
4. 4 Architectural Drawings to be read in conjunction with relevant Engineering Drawings.
5. Standard of Constructions should conform with Architect's and Engineer's Specifications.
6. All critical construction stages should be approved by the Architect or Engineer as relevant.
7. Schedule of Finishes and other Specifications are to be used with these Architectural Drawings. - Refer any discrepancies to the Architect.

DRW: EDISON | OCTOBER 5, 2022 | A102

CHECK: SHLOM | SPACE/2026/04/CH..09



IMAGE 13

CUSTOM

SPACEMERGE® DESIGNS

CLOBEK HERITAGE PLACE,

PROPOSED RESIDENTIAL DEV. @PLOT 1914 SABON-LUGBE EAST EXTENSION,LUGBE,ABUJA

CLOBEK NIG, LTD

NOTES:
1. Do not scale drawings, use figured dimensions only.
2. All dimensions are given in Metric System and to the nearest millimeter (mm).
3. Any discrepancy on site should be referred to the Architect for clarification before proceeding with new works.
4. 4 Architectural Drawings to be read in conjunction with relevant Engineering Drawings.
5. Standard of Constructions should conform with Architect's and Engineer's Specifications.
6. All critical construction stages should be approved by the Architect or Engineer as relevant.
7. Schedule of Finishes and other Specifications are to be used with these Architectural Drawings. - Refer any discrepancies to the Architect.

DRW: EDISON | CHECK: SHLOM | SPACE/2026/04/CH..09

OCTOBER 5, 2022

A 203